



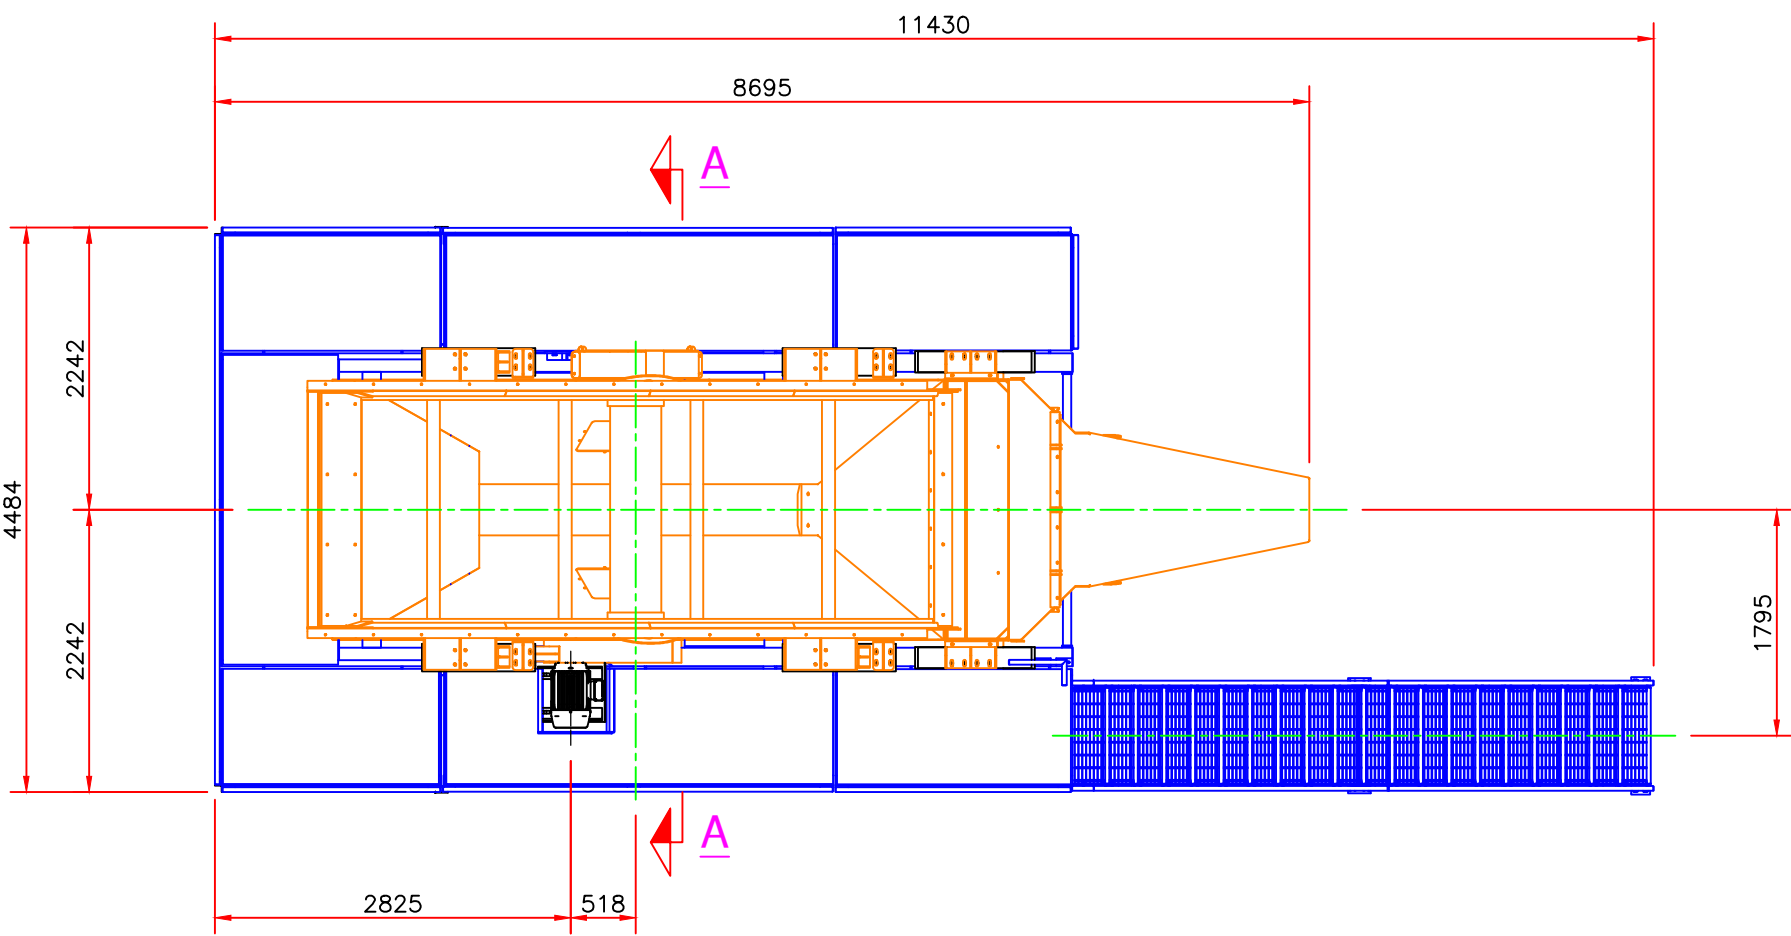

VISTA EN PLANTA

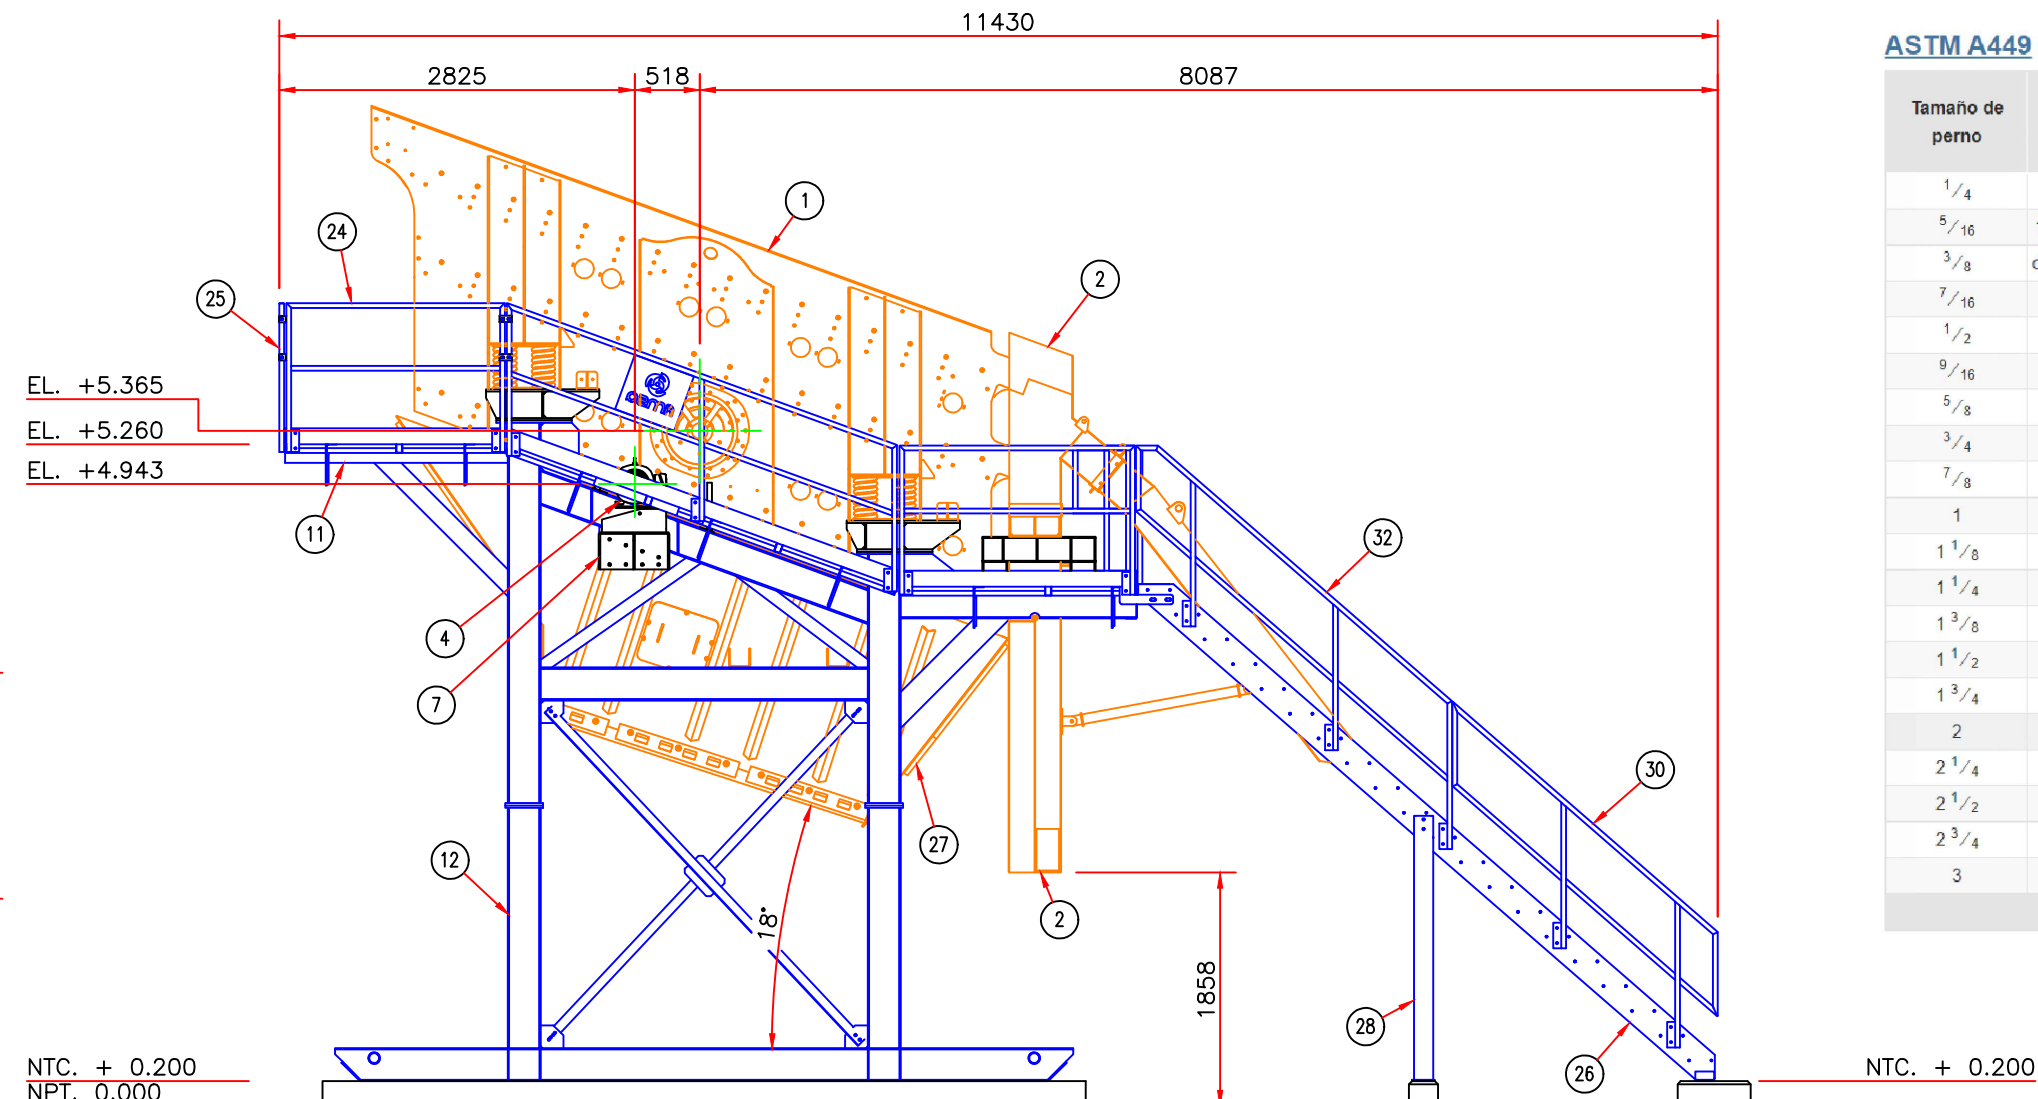



VISTA EN LATERAL

ASTM A449 / SAE Grado 5 *

Tamaño de perno	TPI	Carga de prueba (lb) 1	Carga de la abrazadera (lb) 2	Par de apriete (ft.lbs) 3	Galv + Encerado	Galv Llanura
1/4	20	2,700	2,025	4.4	11	8
5/16	18 años	4,450	3,338	9.9	22	17
3/8	decieses	6,600	4,950	15	39	31
7/16	14	9,050	6,788	25	62.62	40
1/2	13	12,050	9,038	38	94	75
9/16	12	15,450	11,588	54	136	109
5/8	11	19,200	14,400	75	188	150
3/4	10	28,400	21,300	133	333	268
7/8	9.9	39,250	29,438	215	537	429
1	8	51,500	38,625	322	805	644
1 1/8	7.7	56,450	42,338	397	962	794
1 1/4	7.7	71,700	53,775	560	1,400	1,120
1 3/8	6.6	85,450	64,088	734	1,836	1,469
1 1/2	6.6	104,000	78,000	975	2,438	1,950
1 3/4	5.5	104,500	78,375	1,143	2,857	2,286
2	4 1/2	137,500	103,125	1,719	4,267	3,438
2 1/8	4 1/2	178,750	134,063	2,514	6,284	5,027
2 1/2	4.4	220,000	165,000	3,438	8,594	6,875
2 3/4	4.4	271,150	203,363	4,660	11,651	9,321
3	4.4	328,350	246,263	6,157	15,391	12,313

* Los pernos SAE J429 grado 5 no exceden 1-1/2" de diámetro

TRANSMISION	
DESCRIPTION	CANT.
MOTOR ELECTRICO 20 HP 3F 60HZ 440 V 1750 RPM NEMA B HORIZONTAL ARM 256T CONF. F1 MARCA WEG	1
POLEA DE TRANSMISION DE 3RC DE 11.50" DE DIAMETRO EXTERIOR CON BUJE PARA POLEA EN ACERO CALIBRADO A 1 5/8"	1
POLEA CONDUICIA DE 3RC DE 26.625" DE DIAMETRO EXTERIOR CON BUJE 1-5/8"	1
BANDA HERMANADA C-106	3
VELOCIDAD	830 RPM

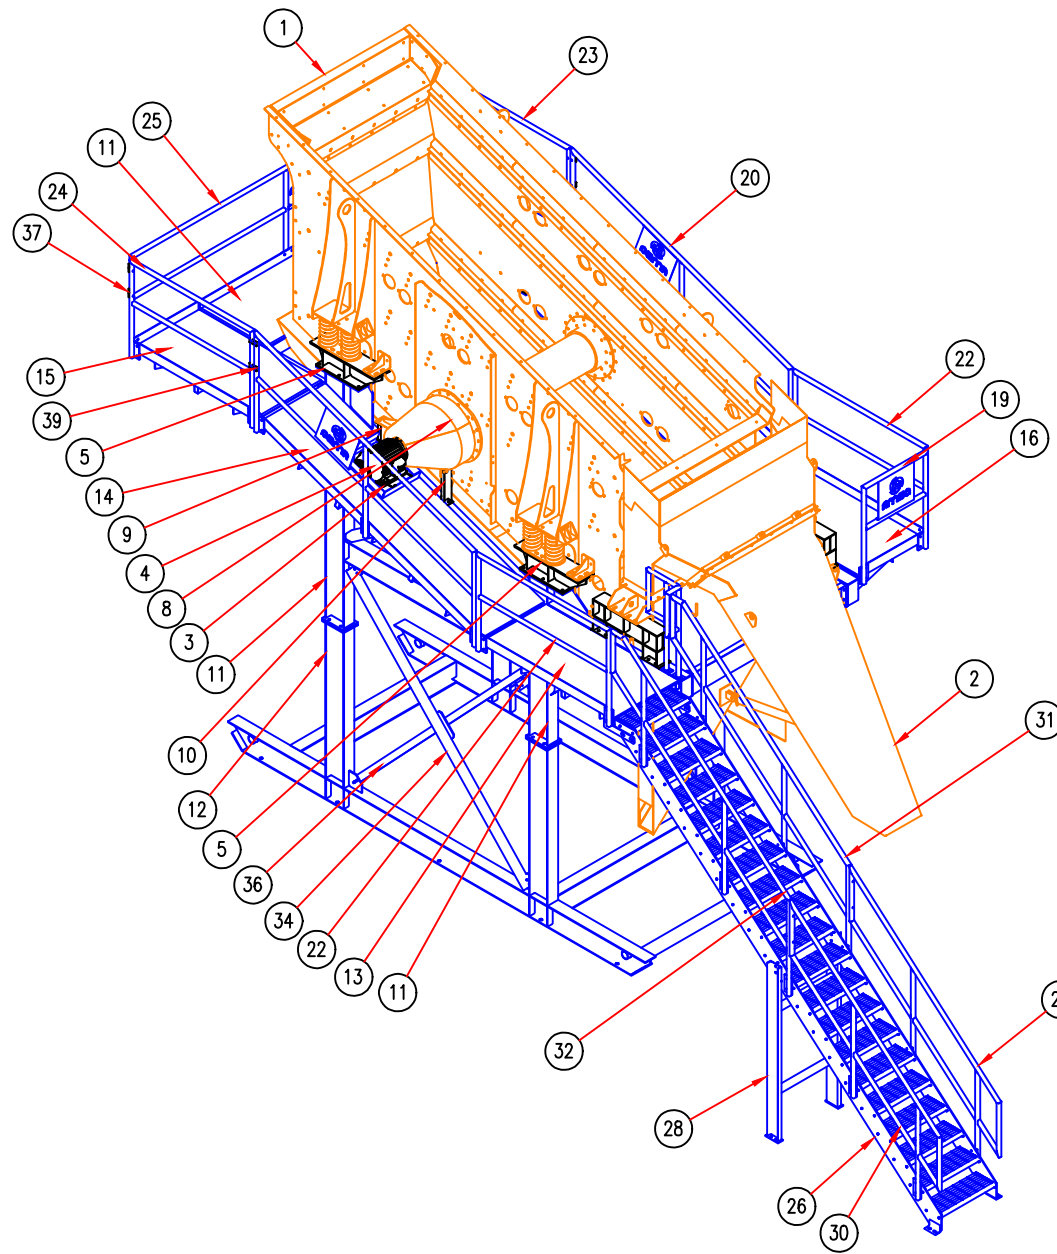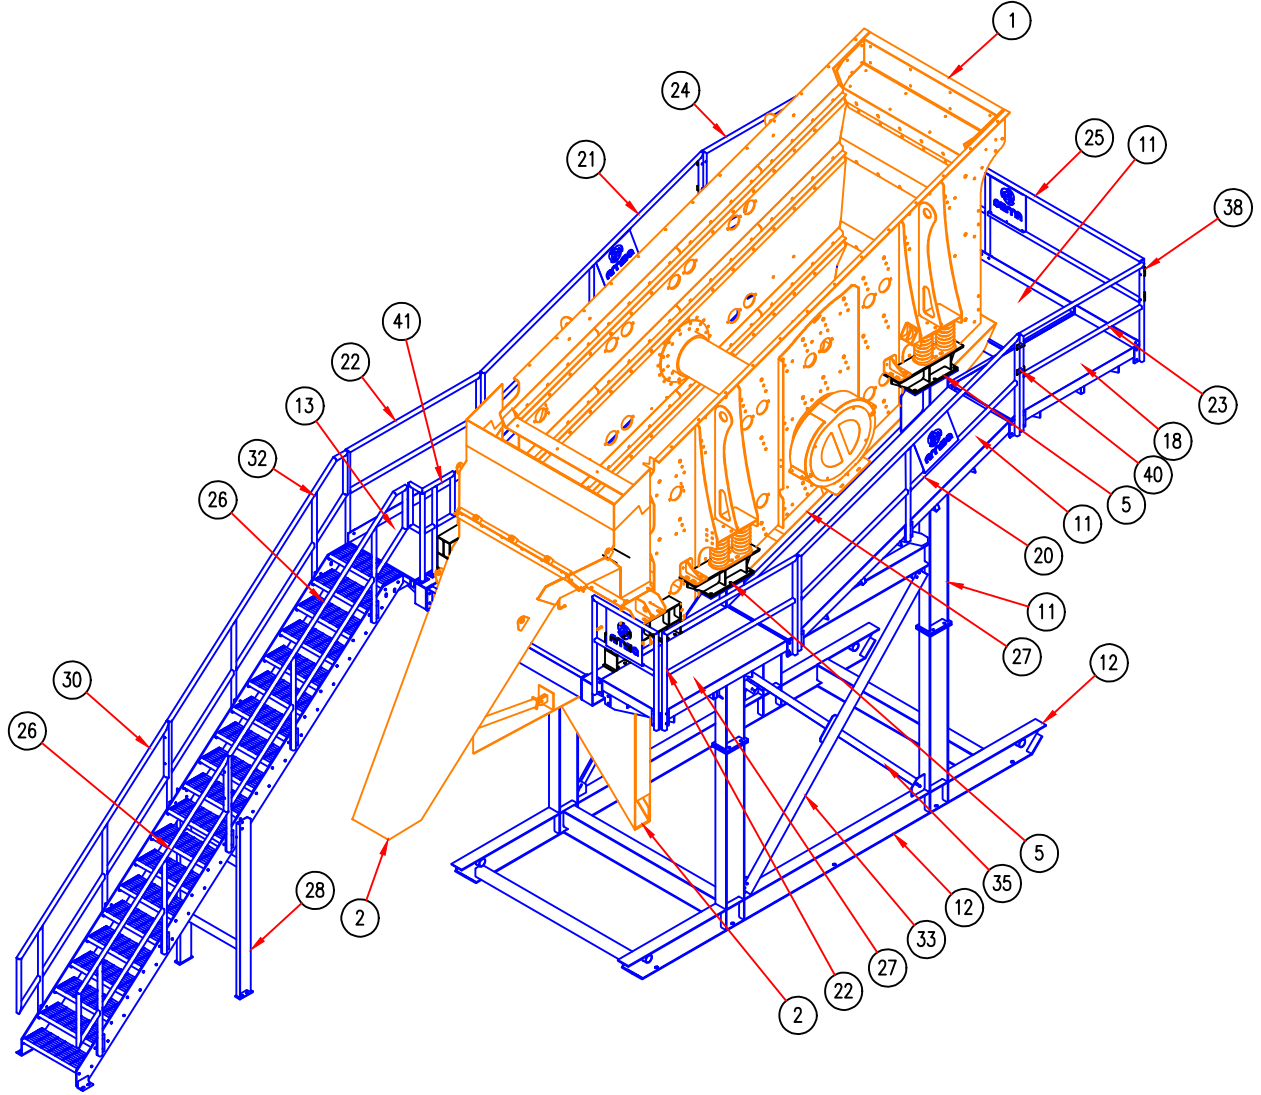

LISTA DE MATERIALES						
N°	No PLANO	No PARTE	CANT.	DESCRIPCION	ANCHO	PESO UNITARIO
1	COMERCIAL	COMERCIAL	1	CRIBA VIBRATORIA 6 x 16 3C SUPERIOR		8738.00
2	X100-13	X100-13	1	CONJUNTO DE CHUTE FRONTAL A BASE DE CHUTE SECCION 1, SECCION 2, SECCION 4, SECCION 5 Y SOPORTE PARA CHUTE FRONTAL		2010.30
3	COMERCIAL	COMERCIAL	1	BASE PM ROSTA		38.00
4	COMERCIAL	COMERCIAL	1	MOTOR ELECTRICO 20 HP 3F 60HZ 440 V 1750 RPM NEMA B HORIZONTAL ARM 256T CONF. F1 MARCA WEG		162.00
5	23002-5-8	23002-5-8	4	BANCO PARA RESORTES DE CV		66.44
6	PIEZA COMERCIAL	PIEZA COMERCIAL	1	POLEA TRANSM. 11.40" EXT 3RC 1.625 INT		17.31
7	23002-2-18	23002-2-18	1	BANCO PM DE CV		66.00
8	23002-2-20	23002-2-20	1	MODIFICACION A GUARDA EXISTENTE DE CV		48.63
9	23002-5-9-2	23002-5-9-2	1	SOPORTE 1 DE GOA TRANS. DE CV		2.41
10	23002-5-9-3	23002-5-9-3	1	SOPORTE 2 DE GOA TRANS. DE CV		3.21
11	23002-5-1-2	23002-5-1-2	1	SECCION 2 SKID		1694.03
12	23002-5-1-1	23002-5-1-1	1	SECCION 1 DE SKID		1008.68
13	23002-5-3-6	23002-5-3-6	1	PASILLO 6 DE SKID		114.60
14	23002-5-3-5	23002-5-3-5	1	PASILLO 5		204.96
15	23002-5-3-4	23002-5-3-4	1	PASILLO 4		123.60
16	23002-5-3-1	23002-5-3-1	1	PASILLO 1		129.48
17	23002-5-3-2	23002-5-3-2	1	PASILLO 2		202.26
18	23002-5-3-3	23002-5-3-3	1	PASILLO 3		107.89
19	23002-5-6-5	23002-5-6-5	1	BARANDAL 5		21.36
20	23002-5-6-2	23002-5-6-2	1	BARANDAL 2		41.15
21	21063-1-6-2	21063-1-6-2	1	BARANDAL 2		44.27
22	23002-5-6-1	23002-5-6-1	2	BARANDAL 1		21.40
23	23002-5-6-3	23002-5-6-3	1	BARANDAL 3		20.51
24	23002-5-6-3	23002-5-6-3	1	BARANDAL 3		20.51
25	23002-5-6-4	23002-5-6-4	1	BARANDAL 4		48.75
26	23002-5-5	23002-5-5	1	ESCALERA		439.49
27	23002-5-2	23002-5-2	1	CHUTE DE FINOS		1433.22
28	23002-5-5A	23002-5-5A	1	SOPORTE PARA ESCALERA		65.38
29	23002-5-6-7	23002-5-6-7	1	BARANDAL 2 ESCALERA		31.03
30	21063-1-6-7	21063-1-6-7	1	BARANDAL 2 ESCALERA		31.03
31	23002-5-6-6	23002-5-6-6	1	BARANDAL 1 ESCALERA		36.97
32	21063-1-6-6	21063-1-6-6	1	BARANDAL 1 ESCALERA		36.97
33	23002-5-1-3	23002-5-1-3	1	SECCION 3 DE SKID		31.04
34	16023-1-1-3	16023-1-1-3	1	SECCION 3 DE SKID		31.04
35	23002-5-1-4	23002-5-1-4	1	SECCION 4 DE SKID		26.59
36	16023-1-1-4	16023-1-1-4	1	SECCION 4 DE SKID		26.59
37	23002-5-6-8	23002-5-6-8	2	SEGURO 1 PARA BARANDAL		0.23
38	21063-1-6-8	21063-1-6-8-1	2	SEGURO 1 PARA BARANDAL		0.23
39	23002-5-6-9	23002-5-6-9	2	SEGURO 2 PARA BARANDAL		0.21
40	21063-1-6-8	21063-1-6-8-2	2	SEGURO 2 PARA BARANDAL		0.21
41	23002-5-6-10	23002-5-6-10	1	BARANDAL 6		16.75
42				TOTAL		17384.33

OT 23-002 SKID 616						O.F. 1983
CANT.	DIAM.	LARGO	COMPLEMENTO	GRADO	UBICACIÓN	NOTA
16	3/4	3	CRPPRYT	5	SKID SECCION 1 CON SECC 2	ROSCA NC, GALV
16	1/2	2	CRPPRYT	5	SKID SECCION 3 CON SECC 4	ROSCA NC, GALV
4	5/8	2	CRPPRYT	5	SOPORTE DE ESCALERA CON ESCALERA	ROSCA NC, GALV
4	3/4	2	CRPPRYT	5	ESCALERA CON PASILLO 6	ROSCA NC, GALV
9	3/4	2	CRPPRYT	5	SKID SECCION 2 CON PASILLO 6	ROSCA NC, GALV
9	5/8	2	CRPPRYT	5	SKID SECCION 2 CON PASILLO 5	ROSCA NC, GALV
8	3/4	2.50	CRPPRYT	5	SKID SECCION 2 CON BANCO PV	ROSCA NC, GALV
4	3/4	2.50	CRPPRYT	5	BANCO CV CON BASE ROSTA	ROSCA NC, GALV
6	5/8	2	CRPPRYT	5	SKID SECCION 2 CON PASILLO 4	ROSCA NC, GALV
6	5/8	2	CRPPRYT	5	SKID SECCION 2 CON PASILLO 3	ROSCA NC, GALV
9	5/8	2	CRPPRYT	5	SKID SECCION 2 CON PASILLO 2	ROSCA NC, GALV
6	3/4	2	CRPPRYT	5	SKID SECCION 2 CON PASILLO 1	ROSCA NC, GALV
2	3/4	3	CRPPRYT	5	CHUTE FRONTAL SECCION 5	ROSCA NC, GALV
16	3/4	2	CRPPRYT	5	SOPORTE CHUTE CON SECCION 5 SKID	ROSCA NC, GALV
8	3/4	2	CRPPRYT	5	SOPORTE CHUTE CON CHUTE	ROSCA NC, GALV
11	3/4	2	CRPPRYT	5	CHUTE SECCION 1 Y SECCION 2	ROSCA NC, GALV
16	5/8	2	CRPPRYT	5	CHUTE SECCION 2 Y SECCION 4	ROSCA NC, GALV
24	3/4	3	CRPPRYT	5	BANCO DE RESORTES CON SECCION 2 SKID	ROSCA NC, GALV
32	3/4	2.50	CRPPRYT	5	BANCO DE RESORTES CON CRIBA	ROSCA NC, GALV
4	5/8	1.50	CRPPRYT	5	SKID SECCION 2 CON SOPORTES GUARDA DE TRANS.	ROSCA NC, GALV
4	5/8	1.50	CRPPRYT	5	SOPORTES GUARDA CON GUARDA DE TRANSMISION	ROSCA NC, GALV
4	3/4	2	CRPPRYT	5	CHUTE DE FINOS CON SKID	ROSCA NC, GALV
16	5/8	2	CRPPRYT	5	CHUTE DE FINOS CON SKID	ROSCA NC, GALV
8	1/2	2	CRPPRYT	5	BARANDAL 2 DE ESCALERA CON ESCALERA	ROSCA NC, GALV
8	1/2	2	CRPPRYT	5	BARANDAL 1 DE ESCALERA CON ESCALERA	ROSCA NC, GALV
8	1/2	2	CRPPRYT	5	BARANDAL 1 CON PASILLO	ROSCA NC, GALV
12	3/8	2	CRPPRYT	5	BARANDAL 2 CON PASILLO	ROSCA NC, GALV
8	1/2	2	CRPPRYT	5	BARANDAL 3 CON PASILLO	ROSCA NC, GALV
8	1/2	2	CRPPRYT	5	BARANDAL 4 CON PASILLO	ROSCA NC, GALV
4	1/2	2	CRPPRYT	5	BARANDAL 5 CON PASILLO	ROSCA NC, GALV
4	1/2	2	CRPPRYT	5	BARANDAL 6 CON SKID	ROSCA NC, GALV
4	5/8	2	CRPPRYT	5	SKID SECCION 2	ROSCA NC, GALV
4	1/2	4	CRPPRYT	5	BARANDAL 1 CON BARANDAL 2 DE ESCALERA	ROSCA NC, GALV
8	1/2	3	CRPPRYT	5	SEGURO 2 BARANDAL CON BARANDAL 3 Y 2	ROSCA NC, GALV
8	1/2	3	CRPPRYT	5	SEGURO 1 BARANDAL CON BARANDAL 3 Y 4	ROSCA NC, GALV
56					CLIPS SILETA PARA REJILLA DE 3/16" X 1/4"	ROSCA NC, GALV
56	1/4	2	CON EMPAQUE	7	PLAS PUNTA DE BIRCA DE 1/4"x2" CON EMPAQUE	GALV

NOTAS GENERALES.

- ESTE PLANO Y SU DISEÑO ES PROPIEDAD DE fimśa Y ES SUMINISTRADO COMO INFORMACIÓN CONFIDENCIAL, NINGUNA PARTE DEL MISMO DEBE SER REPRODUCIDA O UTILIZADA SIN LA AUTORIZACIÓN ESCRITA DE ESTA COMPAÑÍA, SOLO SE UTILIZARÁ COMO REFERENCIA PARA EL TRABAJO INDICADO Y DEBE SER REGRESADO AL ENTREGAR EL MISMO.
- PROHIBIDA CUALQUIER ALTERACIÓN A LOS MATERIALES Y/O DISEÑOS INDICADOS EN ESTE PLANO, SIN LA APROBACIÓN DEL DEPARTAMENTO CORRESPONDIENTE DE fimśa

REVISORES

REV	POR	FECHA
1	ING.	16/03/2023
2	ING.	06/03/2023
3	ING.	24/01/2023

DESCRIPCION

1. ING. 16/03/2023 SE MODIFICÓ TABLA DE TORNILLERÍA

2. ING. 06/03/2023 APROBADO PARA CONSTRUCCION

3. ING. 24/01/2023 PARA REVISION Y/O COMENTARIOS.

DESCRIPCION



TAMAZULIA 285 PARQUE INDUSTRIAL GÓMEZ PALACIO, DGO. C.P. 35070 Tel. (871) 750 00 27 www.fimsa.mx

Cliente ENGECAP HOLDING SA DE CV SOFOM ENR

Dibujó M. CATARINO Proyecto MODULO DE CRIBADO EN SKID

Fecha 24/01/2023 Revisó INC. R. REZA

Aprobó

Título ARREGLO GENERAL DE INSTALACION SKID 616

PED: 4506 OT 23-002

Area OF. 1983

Dibujo No. 23002-5-1

REV.